


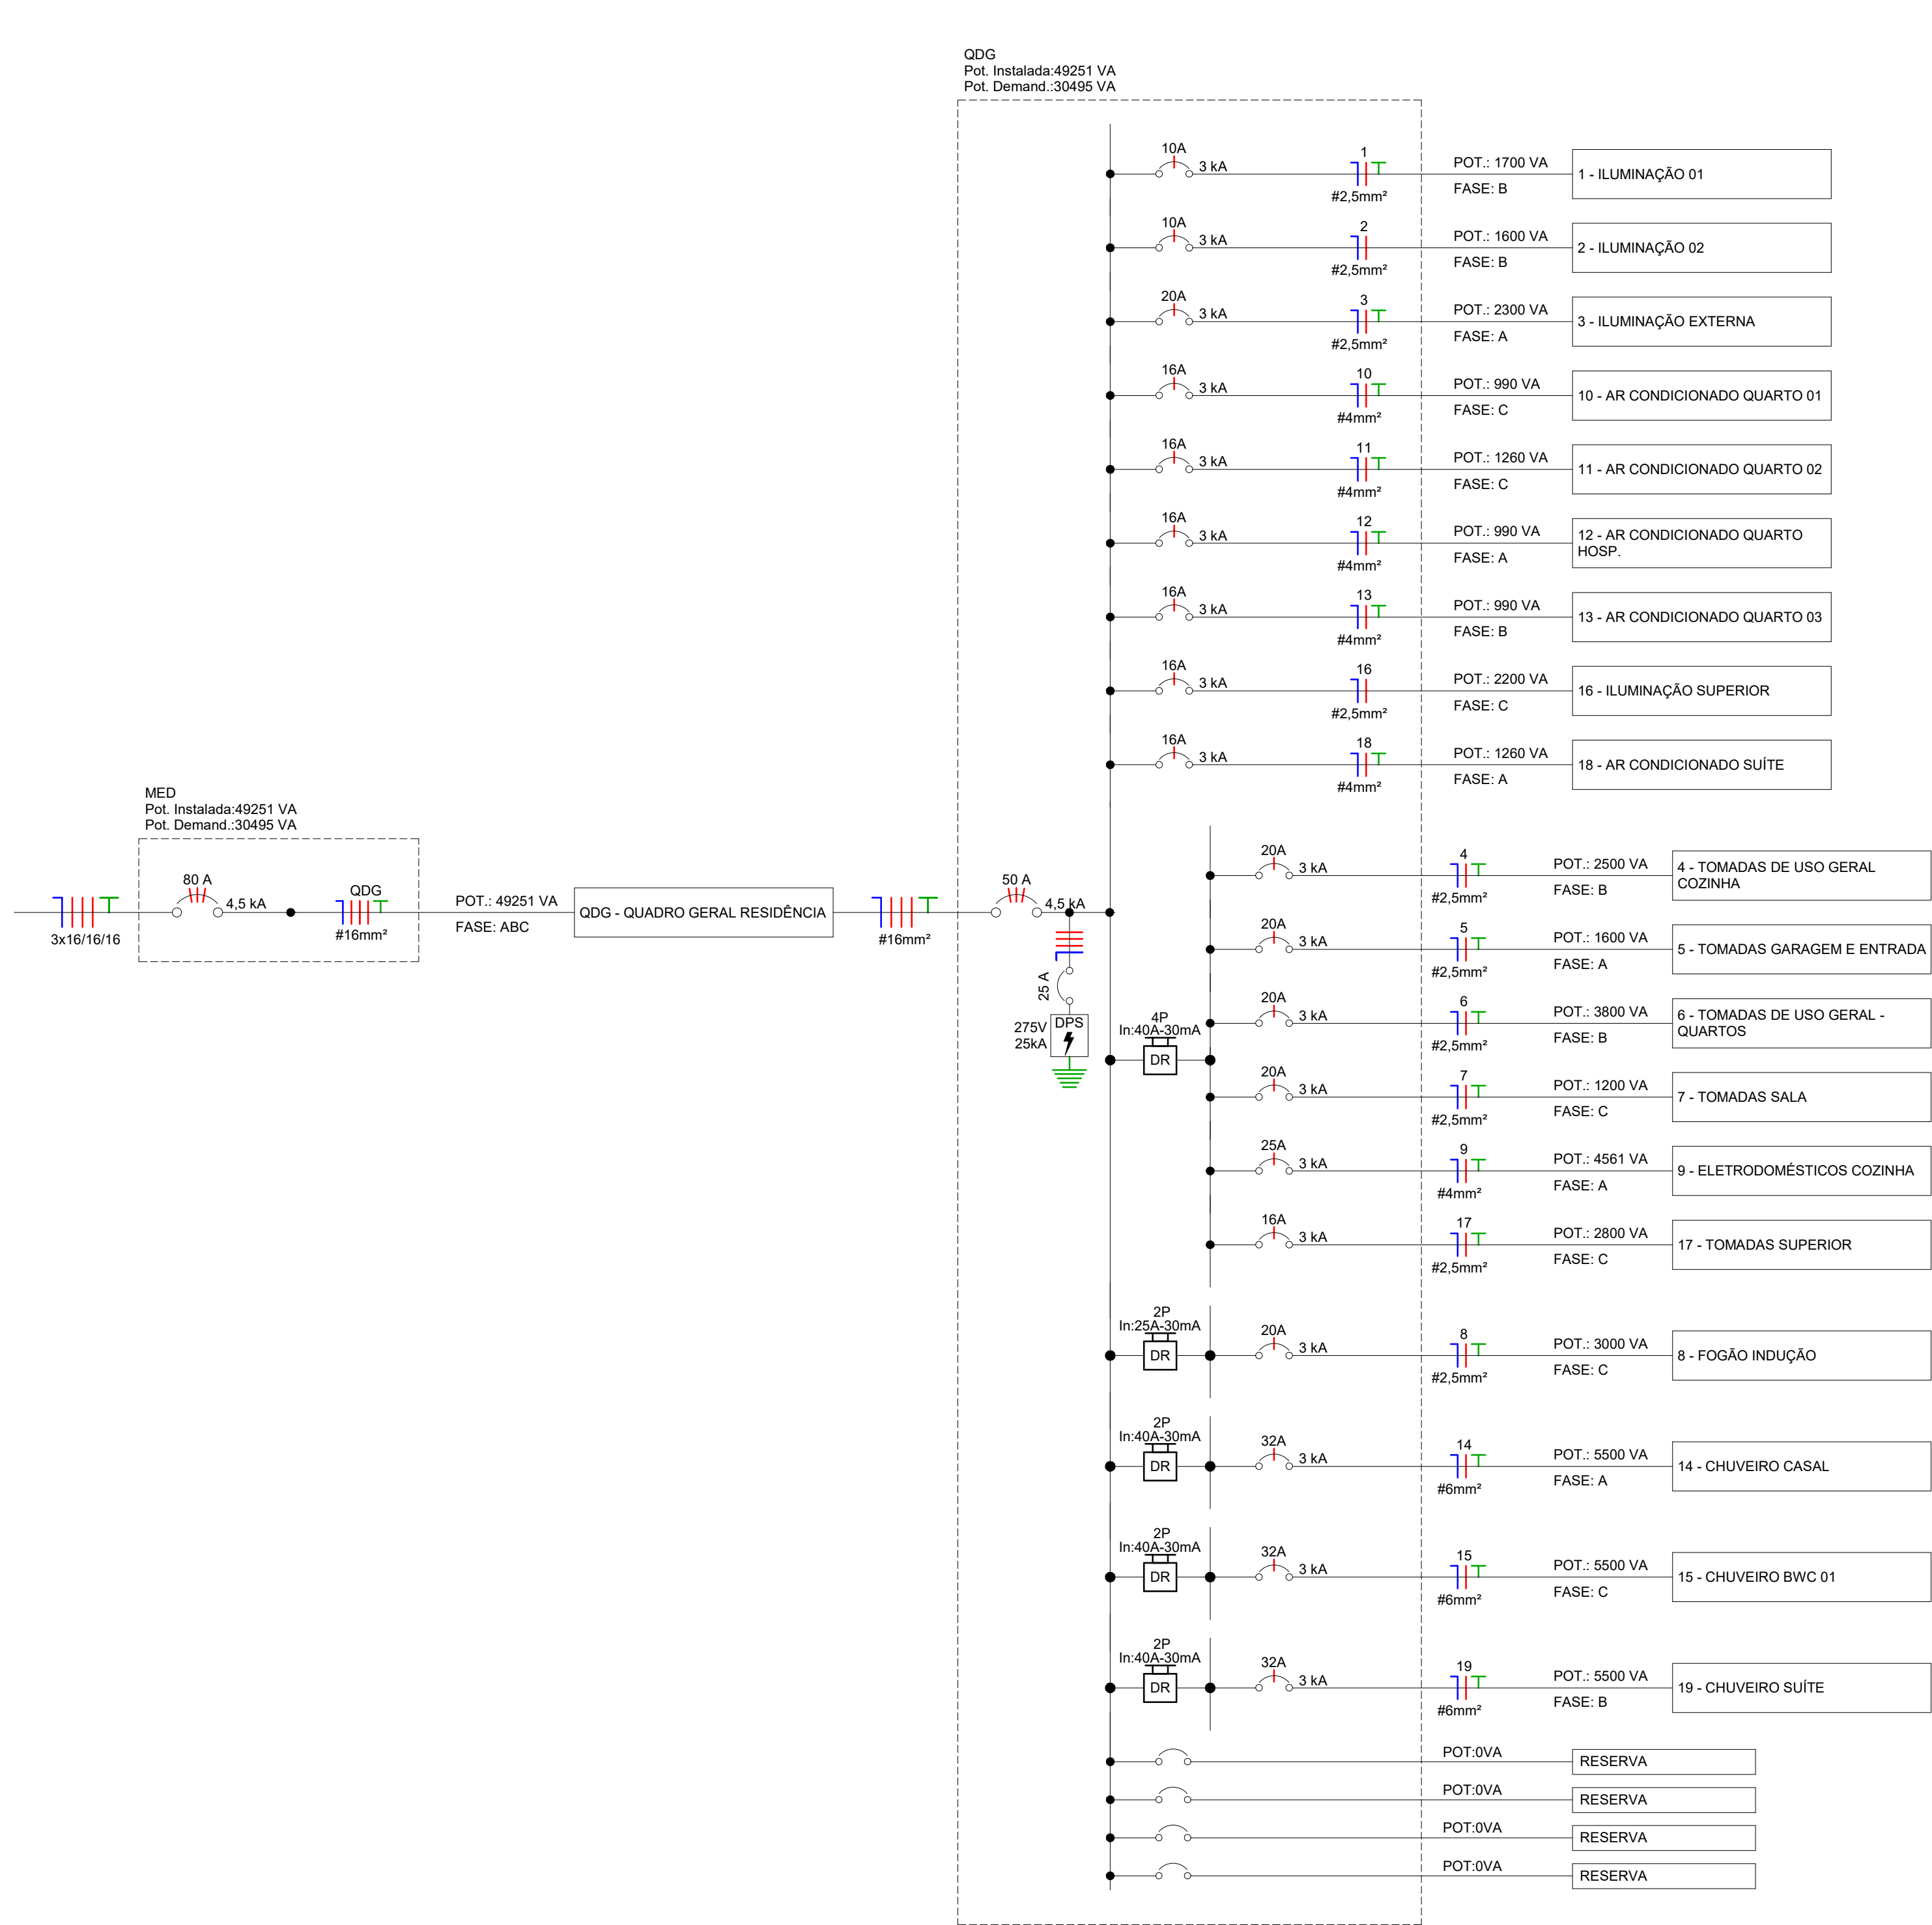

| Listagem de Dispositivos [DGD (TERREO-ELT)] |          |        |
|---------------------------------------------|----------|--------|
| Dispositivo                                 | Dimensão | Quant. |
| Disjuntor DIN Curva B                       | 1P-25A   | 3      |
| Disjuntor DIN Curva C 3 kA                  | 1P-10A   | 2      |
| Disjuntor DIN Curva C 3 kA                  | 7P-16A   | 7      |
| Disjuntor DIN Curva C 3 kA                  | 1P-20A   | 6      |
| Disjuntor DIN Curva C 3 kA                  | 1P-25A   | 1      |
| Disjuntor DIN Curva C 3 kA                  | 1P-32A   | 3      |
| Disjuntor DIN Curva C 4,5 kA                | 3P-50A   | 1      |
| Disjuntor DR 30mA                           | 2P-25A   | 1      |
| Disjuntor DR 30mA                           | 2P-40A   | 3      |
| Disjuntor DR 30mA                           | 4P-40A   | 1      |
| DPS Classe I e II 275V - 275V (Fase)        | 3 25kA   | 3      |
| DPS Classe I e II 275V - 275V (Neutro)      | 2 25kA   | 1      |

| Lista de Materiais - Eletrodutos                                                           |              |                 |                          |
|--------------------------------------------------------------------------------------------|--------------|-----------------|--------------------------|
| Descrição do Material                                                                      | Dímetro (mm) | Comprimento (m) | Referência de Fabricante |
| Eletroduto de PVC Rígido Roscável, em chita, na cor preta, conforme NBR 15465              | 32           | 3,49 m          | Tigre ou equivalente     |
| Eletroduto de PVC Rígido Roscável, em chita, na cor preta, conforme NBR 15465              | 40           | 102,74 m        | Tigre ou equivalente     |
| Eletroduto flexível corrugado PEAD, conforme NBR15715                                      | 40           | 100,00 m        | Tubulone ou equivalente  |
| Eletroduto flexível corrugado PEAD, conforme NBR15715                                      | 25           | 11,21 m         | Tubulone ou equivalente  |
| Eletroduto flexível corrugado Roflex®, em PVC na cor laranja antichamas, conforme NBR15465 | 32           | 5,11 m          | Tigre ou equivalente     |
| Eletroduto flexível corrugado Roflex®, em PVC na cor laranja antichamas, conforme NBR15465 | 25           | 15,81 m         | Tigre ou equivalente     |
| Eletroduto flexível corrugado, em PVC na cor amarelo antichamas, conforme NBR15465         | 32           | 7,00 m          | Tigre ou equivalente     |
| Eletroduto flexível corrugado, em PVC na cor amarelo antichamas, conforme NBR15465         | 25           | 195,11 m        | Tigre ou equivalente     |

Painel: QDG

Sistema de Alimentação: 220/380V Trifásico (3F+N+T)

| Circuito                                               | Descrição                | Inj. Disjuntor (A) | Tipo de Instalação    | Potência Adotada Fase | Potência Adotada 2,5 | Potência Adotada Terra | Esquema  | Cap. de Cond. do... | FCA  | FCT  | FP      | L Considerado | Queda de Tensão %                        | Potência Aparente Fase A | Potência Aparente - Fase B | Potência Aparente - Fase C |
|--------------------------------------------------------|--------------------------|--------------------|-----------------------|-----------------------|----------------------|------------------------|----------|---------------------|------|------|---------|---------------|------------------------------------------|--------------------------|----------------------------|----------------------------|
| 1                                                      | ILUMINAÇÃO 01            | 10,00 A            | [CuiPVC/750V/70"]-U.. | 2,5                   | 2,5                  | 2,5                    | F+N+T    | 31                  | 0,72 | 0,94 | 0,94... | 23,86         | 1,52                                     | 0 VA                     | 1700 VA                    | 0 VA                       |
| 2                                                      | ILUMINAÇÃO 02            | 10,00 A            | [CuiPVC/750V/70"]-U.. | 2,5                   | 2,5                  | 2,5                    | F+N+T    | 31                  | 0,72 | 0,94 | 1       | 17,49         | 1,10                                     | 1600 VA                  | 0 VA                       | 0 VA                       |
| 3                                                      | ILUMINAÇÃO EXTERNA       | 20,00 A            | [CuiPVC/750V/70"]-U.. | 2,5                   | 2,5                  | 2,5                    | F+N+T    | 31                  | 0,72 | 0,94 | 0,95... | 28,32         | 2,47                                     | 2300 VA                  | 0 VA                       | 0 VA                       |
| 4                                                      | TOMADAS DE USO GERAL...  | 20,00 A            | [CuiPVC/750V/70"]-U.. | 2,5                   | 2,5                  | 2,5                    | F+N+T    | 31                  | 0,72 | 0,94 | 0,92    | 17,64         | 1,61                                     | 0 VA                     | 2500 VA                    | 0 VA                       |
| 5                                                      | TOMADAS GARAGEM E        | 20,00 A            | [CuiPVC/750V/70"]-U.. | 2,5                   | 2,5                  | 2,5                    | F+N+T    | 31                  | 0,73 | 0,94 | 0,905   | 13,93         | 0,80                                     | 0 VA                     | 1600 VA                    | 0 VA                       |
| 6                                                      | TOMADAS DE USO GERAL -   | 20,00 A            | [CuiPVC/750V/70"]-U.. | 2,5                   | 2,5                  | 2,5                    | F+N+T    | 31                  | 0,72 | 0,94 | 0,87... | 10,22         | 1,35                                     | 0 VA                     | 3800 VA                    | 0 VA                       |
| 7                                                      | TOMADA SALA              | 20,00 A            | [CuiPVC/750V/70"]-U.. | 2,5                   | 2,5                  | 2,5                    | F+N+T    | 31                  | 0,72 | 0,94 | 0,92    | 17,41         | 0,76                                     | 0 VA                     | 0 VA                       | 1200 VA                    |
| 8                                                      | FOGO INDUÇÃO             | 20,00 A            | [CuiPVC/750V/70"]-U.. | 2,5                   | 2,5                  | 2,5                    | F+N+T    | 31                  | 0,72 | 0,94 | 1       | 17,56         | 2,08                                     | 0 VA                     | 0 VA                       | 3000 VA                    |
| 9                                                      | ELETRDOMÉSTICOS...       | 25,00 A            | [CuiPVC/750V/70"]-U.. | 4                     | 4                    | 4                      | F+N+T    | 41                  | 0,72 | 0,94 | 0,92    | 16,73         | 1,73                                     | 4561 VA                  | 0 VA                       | 0 VA                       |
| 10                                                     | AR CONDICIONADO QUART... | 16,00 A            | [CuiPVC/750V/70"]-U.. | 4                     | 4                    | 4                      | F+N+T    | 41                  | 0,73 | 0,94 | 0,9     | 4,16          | 0,09                                     | 990 VA                   | 0 VA                       | 0 VA                       |
| 11                                                     | AR CONDICIONADO QUART... | 16,00 A            | [CuiPVC/750V/70"]-U.. | 4                     | 4                    | 4                      | F+N+T    | 41                  | 0,72 | 0,94 | 0,9     | 11,91         | 0,33                                     | 1260 VA                  | 0 VA                       | 0 VA                       |
| 12                                                     | AR CONDICIONADO QUART... | 16,00 A            | [CuiPVC/750V/70"]-U.. | 4                     | 4                    | 4                      | F+N+T    | 41                  | 0,73 | 0,94 | 0,9     | 15,37         | 0,34                                     | 0 VA                     | 0 VA                       | 990 VA                     |
| 13                                                     | AR CONDICIONADO QUART... | 16,00 A            | [CuiPVC/750V/70"]-U.. | 4                     | 4                    | 4                      | F+N+T    | 41                  | 0,72 | 0,94 | 0,9     | 18,44         | 0,41                                     | 0 VA                     | 990 VA                     | 0 VA                       |
| 14                                                     | CHUVEIRO CASAL           | 32,00 A            | [CuiPVC/750V/70"]-U.. | 6                     | 6                    | 6                      | F+N+T    | 53                  | 0,72 | 0,94 | 1       | 4,79          | 0,43                                     | 0 VA                     | 0 VA                       | 5500 VA                    |
| 15                                                     | CHUVEIRO DWY 01          | 32,00 A            | [CuiPVC/750V/70"]-U.. | 6                     | 6                    | 6                      | F+N+T    | 53                  | 0,72 | 0,94 | 1       | 4,98          | 0,45                                     | 0 VA                     | 0 VA                       | 5500 VA                    |
| 16                                                     | ILUMINAÇÃO SUPERIOR      | 16,00 A            | [CuiPVC/750V/70"]-U.. | 2,5                   | 2,5                  | 2,5                    | F+N+T    | 24                  | 0,73 | 0,94 | 0,98... | 18,25         | 1,56                                     | 0 VA                     | 0 VA                       | 2200 VA                    |
| 17                                                     | ILUMINAÇÃO SUPERIOR      | 16,00 A            | [CuiPVC/750V/70"]-U.. | 2,5                   | 2,5                  | 2,5                    | F+N+T    | 24                  | 0,73 | 0,94 | 0,96    | 15,95         | 1,53                                     | 0 VA                     | 0 VA                       | 2800 VA                    |
| 18                                                     | AR CONDICIONADO SUITE    | 16,00 A            | [CuiPVC/750V/70"]-U.. | 4                     | 4                    | 4                      | F+N+T    | 32                  | 0,73 | 0,94 | 0,9     | 12,11         | 0,34                                     | 0 VA                     | 0 VA                       | 1200 VA                    |
| 19                                                     | CHUVEIRO SUITE           | 32,00 A            | [CuiPVC/750V/70"]-U.. | 6                     | 6                    | 6                      | F+N+T    | 53                  | 0,72 | 0,94 | 1       | 6,37          | 0,57                                     | 5500 VA                  | 0 VA                       | 0 VA                       |
| 20                                                     |                          |                    |                       |                       |                      |                        |          |                     |      |      |         |               |                                          |                          |                            |                            |
| 21                                                     |                          |                    |                       |                       |                      |                        |          |                     |      |      |         |               |                                          |                          |                            |                            |
| 22                                                     |                          |                    |                       |                       |                      |                        |          |                     |      |      |         |               |                                          |                          |                            |                            |
| 23                                                     |                          |                    |                       |                       |                      |                        |          |                     |      |      |         |               |                                          |                          |                            |                            |
| 24                                                     |                          |                    |                       |                       |                      |                        |          |                     |      |      |         |               |                                          |                          |                            |                            |
| 25                                                     |                          |                    |                       |                       |                      |                        |          |                     |      |      |         |               |                                          |                          |                            |                            |
| Classificação da Carga                                 |                          |                    |                       |                       |                      |                        |          |                     |      |      |         |               | Totais                                   | 16211 VA                 | 16090 VA                   | 18950 VA                   |
| Equatorial - Iluminação + TUGs (Residencial)           |                          |                    |                       | 1880 VA               | 0,45                 |                        | 8910 VA  |                     |      |      |         |               |                                          | Totais do Painel         |                            |                            |
| Equatorial - Ar Condicionado Residencial               |                          |                    |                       | 5490 VA               | 0,78                 |                        | 4282 VA  |                     |      |      |         |               | Potência Total Instalada: 49251 VA       |                          |                            |                            |
| Equatorial - Chuveiros                                 |                          |                    |                       | 16500 VA              | 0,67                 |                        | 11055 VA |                     |      |      |         |               | Potência Total Demandada: 30495 VA       |                          |                            |                            |
| Equatorial - Eletrodomésticos                          |                          |                    |                       | 1200 VA               | 0,75                 |                        | 900 VA   |                     |      |      |         |               | Corrente Total Instalada: 74,82 A        |                          |                            |                            |
| Equatorial - Fogão Elétrico                            |                          |                    |                       | 3000 VA               | 1,00                 |                        | 3000 VA  |                     |      |      |         |               | Corrente Total Demandada: 46,83 A        |                          |                            |                            |
| Equatorial - Secadora, Lava-Louças, Forno e Microondas |                          |                    |                       | 3261 VA               | 0,72                 |                        | 2348 VA  |                     |      |      |         |               | Fator de Demanda Total do Quadro: 61,93% |                          |                            |                            |
| Notas:                                                 |                          |                    |                       |                       |                      |                        |          |                     |      |      |         |               |                                          |                          |                            |                            |

| Quadro de Cargas                                                                 |  |                                
|----------------------------------------------------------------------------------|--|--------------------------------|-----|-----|-----|-----|-----|------|-----|-----|--------|--------|--------|---------|-------|---------|---------|----------|----------|-------|--------|----------|--------|---------|--------|----------|-------|-------|-------|-------|---------|
| ODG                                                                              |  |                                
| Ckr.                                                                             |  | Descrição                      | V   |     |     |     |     |      |     |     | Esqmts | Tensão | Pot. V | Pot. VA |       | Demanda | Fase    | I A      | A        | Fases | Pot. A | Cont. m² | Fase A | Fase B  | Fase C | Fase ABC | FCA   | FCT   |       |       |         |
|                                                                                  |  |                                | 46W | 54W | 80W | 90W | 90W | 100W | 50W | 89W |        |        |        | 1134W   | 1500W |         |         |          |          |       |        |          |        |         |        |          |       |       | 3000W | 5500W | Pot. VA |
| 1                                                                                |  | ILUMINAÇÃO 01                  |     |     |     |     |     | 1    | 5   |     |        |        | FNT    | 220     | 1607  | 765     | 45      | 0,95     | 3,48     | 1     | 10     | 2,5      |        | 1700    | B      |          | 0,72  | 0,94  |       |       |         |
| 2                                                                                |  | ILUMINAÇÃO 02                  |     |     |     |     |     | 16   | 23  |     |        |        | FNT    | 220     | 1600  | 720     | 45      | 1        | 3,27     | 1     | 10     | 2,5      | 1600   |         | A      |          | 0,72  | 0,94  |       |       |         |
| 3                                                                                |  | ILUMINAÇÃO EXTERNA             |     |     |     |     |     |      |     |     |        |        | FNT    | 220     | 2200  | 1035    | 45      | 0,96     | 4,7      | 1     | 20     | 2,5      | 2300   |         | A      |          | 0,72  | 0,94  |       |       |         |
| 4                                                                                |  | TOMADAS DE USO GERAL COZINHA   |     |     | 7   |     |     | 3    |     |     |        |        | FNT    | 220     | 2200  | 1125    | 45      | 0,92     | 5,11     | 1     | 20     | 2,5      |        | 2500    | B      |          | 0,72  | 0,94  |       |       |         |
| 5                                                                                |  | TOMADAS GARAGEM E ENTRADA      |     |     | 2   | 14  |     |      |     |     |        |        | FNT    | 220     | 1448  | 720     | 45      | 0,9      | 3,27     | 1     | 20     | 2,5      |        | 1600    | B      |          | 0,73  | 0,94  |       |       |         |
| 6                                                                                |  | TOMADAS DE USO GERAL - QUARTOS |     |     | 14  |     |     | 4    |     |     |        |        | FNT    | 220     | 3328  | 1710    | 45      | 0,88     | 7,77     | 1     | 20     | 2,5      |        | 3800    | B      |          | 0,72  | 0,94  |       |       |         |
| 7                                                                                |  | TOMADAS SALA                   |     |     |     | 12  |     |      |     |     |        |        | FNT    | 220     | 1104  | 540     | 45      | 0,92     | 2,45     | 1     | 20     | 2,5      |        | 1200    | C      |          | 0,72  | 0,94  |       |       |         |
| 8                                                                                |  | FOGO INDUÇÃO                   |     |     |     |     |     |      |     |     |        |        | FNT    | 220     | 3000  | 1500    | 100     | 1        | 13,64    | 1     | 20     | 2,5      |        | 1200    | C      |          | 0,72  | 0,94  |       |       |         |
| 9                                                                                |  | ELETRODOMESTOS COZINHA         |     |     |     |     |     | 1    | 2   |     |        | 2      | 1      | FNT     | 220   | 4195,99 | 3292,82 | 72,2     | 0,92     | 14,97 | 1      | 25       | 4      | 4500,86 |        | A        |       | 0,72  | 0,94  |       |         |
| 10                                                                               |  | AR CONDICIONADO QUARTO 01      |     |     |     |     |     |      |     |     |        | 1      |        | FNT     | 220   | 891     | 772,2   | 78       | 0,9      | 3,51  | 1      | 16       | 4      | 990     |        | A        |       | 0,73  | 0,94  |       |         |
| 11                                                                               |  | AR CONDICIONADO QUARTO 02      |     |     |     |     |     |      |     |     |        |        | 1      |         | FNT   | 220     | 1134    | 962,8    | 78       | 0,9   | 4,47   | 1        | 16     | 4       | 1280   |          | A     |       | 0,72  | 0,94  |         |
| 12                                                                               |  | AR CONDICIONADO QUARTO HOSP.   |     |     |     |     |     |      |     |     |        |        |        | FNT     | 220   | 891     | 772,2   | 78       | 0,9      | 3,51  | 1      | 16       | 4      | 990     | C      |          | 0,73  | 0,94  |       |       |         |
| 13                                                                               |  | AR CONDICIONADO QUARTO 03      |     |     |     |     |     |      |     |     |        |        |        | FNT     | 220   | 891     | 772,2   | 78       | 0,9      | 3,51  | 1      | 16       | 4      | 990     | B      |          | 0,72  | 0,94  |       |       |         |
| 14                                                                               |  | CHUVEIRO CASAL                 |     |     |     |     |     |      |     |     |        |        | 1      | FNT     | 220   | 5500    | 3685    | 67       | 1        | 16,75 | 1      | 32       | 6      | 5500    | C      |          | 0,72  | 0,94  |       |       |         |
| 15                                                                               |  | CHUVEIRO RWG 01                |     |     |     |     |     |      |     |     |        |        |        | FNT     | 220   | 5500    | 3685    | 67       | 1        | 16,75 | 1      | 32       | 6      | 5500    | B      |          | 0,72  | 0,94  |       |       |         |
| 16                                                                               |  | ILUMINAÇÃO SUPERIOR            |     |     |     |     |     |      | 17  | 1   |        |        |        | FNT     | 220   | 2160    | 990     | 45       | 0,98     | 4,5   | 1      | 16       | 2,5    |         | 2200   | C        |       | 0,73  | 0,94  |       |         |
| 17                                                                               |  | TOMADAS SUPERIOR               |     |     |     |     |     |      |     |     |        |        |        | FNT     | 220   | 2408    | 1260    | 45       | 0,86     | 5,73  | 1      | 16       | 2,5    |         | 2800   | C        |       | 0,73  | 0,94  |       |         |
| 18                                                                               |  | ILUMINAÇÃO SUITE               |     |     |     |     |     |      |     |     |        |        | 1      | FNT     | 220   | 1134    | 962,8   | 78       | 0,9      | 4,47  | 1      | 16       | 4      |         | 1280   | C        |       | 0,73  | 0,94  |       |         |
| 19                                                                               |  | CHUVEIRO SUITE                 |     |     |     |     |     |      |     |     |        |        |        | 1       | FNT   | 220     | 5500    | 3685     | 67       | 1     | 16,75  | 1        | 32     | 6       | 5500   |          | A     |       | 0,72  | 0,94  |         |
| Total                                                                            |  |                                |     |     | 20  | 32  | 40  | 1    | 61  | 10  | 3      | 2      | 2      | 1       | 3     | FFNT    | 380     | 46791,99 | 30465,02 | 61,9  | 0,95   | 46,33    | 3      | 50      | 16     | 16210,86 | 16090 | 16950 | ABC   | 0,72  | 0,94    |
| Total Alim.                                                                      |  |                                
| Potência Total (46791,99 W) (49250,86 VA)   Potência Demandada: 61.9% (30495 VA) |  |                                

| Lista de Materiais - Componentes   |                             |                    |                                          |
|---|-----------------------------|--------------------|------------------------------------------|
| Descrição do Material   | Dimensões                   | Quantidade (peças) | Referência Fabricante                    |
| Pendente Linear - Luminária LED   |                             | 1                  |                                          |
| Conector de Distribuição Tígrise para até 36 derivações de Embutir   | 525,00 x 250,00 x 313,00 mm | 1                  | TIGRE                                    |
| <b>Caixas de Embutir</b>   |                             |                    |                                          |
| Caixa de Luz 4"2x2, de material em PVC na cor amarela para eletroduto corrugado                                                                                           | 4"2x2"                      | 68                 | Tigre Linhas Tigreflex ou equivalente    |
| Caixa de Piso Baixa 4"2, de alumínio, 3/4"   | 4"2x2"                      | 5                  | Tigre Linhas Tigreflex ou equivalente    |
| Caixa odológica 4"x4" com fundo móvel, em PVC na cor amarela para eletroduto corrugado                                                                                    | 4"x4"                       | 19                 | Tigre Linhas Tigreflex ou equivalente    |
| <b>Condutores de PVC</b>   |                             |                    |                                          |
| Condutores de PVC multilaminados na cor cinza, Ø1", sem Tampa, com 5 entradas                                                                                             |                             | 36                 | Tigre, Linha Conduite Top ou equivalente |
| Tampa Copa para Conduite Top de PVC multilaminado na cor cinza   |                             | 44                 | Tigre, Linha Conduite Top ou equivalente |
| <b>Conexões de Eletrocalha</b>   |                             |                    |                                          |
| Parafuso Cabeça de Lenthita com Tampa, Ø1" (1/2") com Unid. único, Para Eletrocalha, Chapa de aço carbono galvanizado, largura de 78 mm altura de 116 mm                  |                             | 40                 | Perfi-Lidur ou equivalente               |
| <b>Derivações de Eletrocalha</b>   |                             |                    |                                          |
| Curva Horizontal 90°, para eletrocalha, chapa de aço carbono galvanizado, largura 50 mm altura da aba 50 mm                                                               | 50x50mm                     | 2                  | Poleoduto ou equivalente                 |
| Curva Vertical 90°, para eletrocalha, chapa de aço carbono galvanizado, largura 50 mm e altura da aba 50 mm                                                               | 50x50mm                     | 1                  | Poleoduto ou equivalente                 |
| Curva Vertical Esterna 90°, para eletrocalha, chapa de aço carbono galvanizado, largura 100 mm e altura da aba 50 mm                                                      | 100x50mm                    | 1                  | Poleoduto ou equivalente                 |
| Terminal de Fechamento, para eletrocalha, de chapa de aço carbono galvanizado, largura de 50 mm altura da aba 50 mm                                                       | 50x50mm                     | 8                  | Poleoduto ou equivalente                 |
| Terminal de Fechamento, para eletrocalha, de chapa de aço carbono galvanizado, largura de 100 mm altura da aba 50 mm                                                      | 100x50mm                    | 1                  | Poleoduto ou equivalente                 |
| <b>Derivações de Eletrodutos</b>   |                             |                    |                                          |
| Unid. único para eletroduto de diâmetro nominal 25, rosca BSP Ø1"   | Ø1"                         | 17                 | Daiwa ou equivalente                     |
| Unid. único para eletroduto de diâmetro nominal 32, rosca BSP Ø1,14"   | Ø1,14"                      | 2                  | Daiwa ou equivalente                     |
| Unid. único para eletroduto de diâmetro nominal 40, rosca BSP Ø1,31"   | Ø1,31"                      | 2                  | Daiwa ou equivalente                     |
| <b>Derivações de Perfilados</b>   |                             |                    |                                          |
| Caixa para tomada para instalação em perfilado de 38 x 38mm, de chapa de aço carbono galvanizado, com Tampa e parafusado, largura de 50 mm altura de 78 mm e profundidade | 38 x 38 mm                  | 22                 | Poleoduto ou equivalente                 |
| Junção Horizontal Interna 1", para perfilado de 38 x 38mm, de chapa de aço carbono galvanizado                                                                            | 38 x 38 mm                  | 1                  | Poleoduto ou equivalente                 |
| Junção Horizontal Interna 7/8", para perfilado de 38 x 38mm, de chapa de aço carbono galvanizado                                                                          | 38 x 38 mm                  | 4                  | Poleoduto ou equivalente                 |
| Saída lateral para perfilado, para perfilado de 38 x 38mm, de chapa de aço carbono galvanizado                                                                            | 38 x 38 mm                  | 10                 | Poleoduto ou equivalente                 |
| Saída lateral para perfilado, para perfilado de 38 x 38mm, de chapa de aço carbono galvanizado                                                                            | 38 x 38 mm                  | 14                 | Poleoduto ou equivalente                 |
| <b>Derivações para Eletroduto de PVC Rígido</b>   |                             |                    |                                          |
| Unid. 90° para eletroduto rígido de PVC, DN25mm, rosca Ø3/4" BSP conforme ABNT NBR 15465                                                                                  | DN25mm (3/4")               | 3                  | Tigre/Daiwa ou equivalente               |
| Unid. 90° para eletroduto rígido de PVC, DN25mm, rosca Ø3/4" BSP conforme ABNT NBR 15465                                                                                  | DN25mm (3/4")               | 4                  | Tigre/Daiwa ou equivalente               |
| Unid. 90° para eletroduto rígido de PVC, DN25mm, rosca Ø1" BSP conforme ABNT NBR 15465                                                                                    | DN25mm (1")                 | 4                  | Tigre/Daiwa ou equivalente               |
| Unid. 90° para eletroduto rígido de PVC, DN25mm, rosca Ø1" BSP conforme ABNT NBR 15465                                                                                    | DN25mm (1")                 | 94                 | Tigre ou equivalente                     |
| Unid. 90° para eletroduto rígido de PVC, DN25mm, rosca Ø1" BSP conforme ABNT NBR 15465                                                                                    | DN25mm (1")                 | 8                  | Tigre ou equivalente                     |
| <b>Fixações de Eletrocalhas</b>   |                             |                    |                                          |
| Anelax para fixação de eletrocalha, galvanizada Ø1/4"   | Ø1/4"                       | 40                 | Perfi-Lidur ou Equivalente Técnico       |
| Parafuso cabeça lenthita auto travante, galvanizado, Ø1/4"   | Ø1/4"                       | 40                 | Poleoduto ou similar                     |
| <b>Fixações de Perfilados</b>   |                             |                    |                                          |
| Pino sextavado de aço carbono, galvanizada, Ø1/4"   | Ø1/4"                       | 40                 | Perfi-Lidur ou equivalente               |
| <b>Fixações Elétricas</b>   |                             |                    |                                          |
| Anelax de ferro fundido, com galvanização eletrolítica, para fixação de eletroduto rígido metálico de diâmetro nominal 25, rosca Ø1" BSP                                  | Ø1"                         | 15                 | Canoas ou equivalente                    |
| Anelax Ø1/4", de aço carbono, galvanizado   | Ø1/4"                       | 44                 | Poleoduto ou equivalente                 |
| Anelax Ø3/8", de aço carbono, galvanizado   | Ø3/8"                       | 15                 | Poleoduto ou equivalente                 |
| Bucha metálica, de ferro fundido com galvanização a fogo, para eletroduto rígido metálico de diâmetro nominal 25, rosca Ø1" BSP                                           | Ø3/8"                       | 28                 | Bloco ou equivalente                     |
| Junção Horizontal Externa, rosca Ø3/8", de aço carbono, galvanizado, tipo GB                                                                                              | Ø3/8"                       | 26                 | Poleoduto ou equivalente                 |
| Garcho para perfilado, aço galvanizado, 38x38mm   | 38x38mm                     | 11                 | Poleoduto ou equivalente                 |
| Parafuso cabeça de lenthita auto travante, de aço carbono, galvanizado, rosca Ø3/8", perfilado 3/4"                                                                       | Ø3/8" x 3/4"                | 88                 | Poleoduto ou equivalente                 |
| Perfilado Perfilado para Suportes, de chapa de aço carbono galvanizado, 38 mm de largura 38 mm altura da aba 250 mm de comprimento                                        | 38x38x 200 mm               | 4                  | Poleoduto ou equivalente                 |
| Perfilado Perfilado para Suportes, de chapa de aço carbono galvanizado, 38 mm de largura 38 mm altura da aba 250 mm de comprimento                                        | 38x38x 250 mm               | 4                  | Poleoduto ou equivalente                 |
| Pino longitudinal com pino requerido, de aço carbono, galvanização eletrolítica, rosca Ø 1/4"                                                                             | Ø1/4"                       | 44                 | Poleoduto ou equivalente                 |
| Pino longitudinal com pino requerido, de aço carbono, galvanização eletrolítica, rosca Ø 3/8"                                                                             | Ø3/8"                       | 28                 | Poleoduto ou equivalente                 |
| Pino sextavado, rosca Ø1/4", de aço carbono, galvanizado   | Ø1/4"                       | 44                 | Poleoduto ou equivalente                 |
| Pino sextavado, rosca Ø3/8", de aço carbono galvanizado   | Ø3/8"                       | 230                | Poleoduto ou equivalente                 |
| Verghalho com rosca total de aço, galvanizado, rosca Ø3/8" x 250 mm de comprimento                                                                                        | Ø3/8" x 250 mm              | 2                  | Poleoduto ou equivalente                 |
| Verghalho com rosca total de aço, galvanizado, rosca Ø3/8" x 300 mm de comprimento                                                                                        | Ø3/8" x 300 mm              | 2                  | Poleoduto ou equivalente                 |
| Verghalho com rosca total de aço, galvanizado, rosca Ø3/8" x 475 mm de comprimento                                                                                        | Ø3/8" x 475 mm              | 2                  | Poleoduto ou equivalente                 |
| Verghalho com rosca total de aço, galvanizado, rosca Ø3/8" x 500 mm de comprimento                                                                                        | Ø3/8" x 500 mm              | 1                  | Poleoduto ou equivalente                 |
| Verghalho com rosca total de aço, galvanizado, rosca Ø3/8" x 550 mm de comprimento                                                                                        | Ø3/8" x 550 mm              | 8                  | Poleoduto ou equivalente                 |
| Verghalho com rosca total de aço, galvanizado, rosca Ø3/8" x 750 mm de comprimento                                                                                        | Ø3/8" x 750 mm              | 1                  | Poleoduto ou equivalente                 |
| Verghalho com rosca total de aço, galvanizado, rosca Ø3/8" x 825 mm de comprimento                                                                                        | Ø3/8" x 825 mm              | 2                  | Poleoduto ou equivalente                 |
| Verghalho com rosca total de aço, galvanizado, rosca Ø3/8" x 1050 mm de comprimento                                                                                       | Ø3/8" x 1050 mm             | 1                  | Poleoduto ou equivalente                 |
| Verghalho com rosca total de aço, galvanizado, rosca Ø3/8" x 1175 mm de comprimento                                                                                       | Ø3/8" x 1175 mm             | 2                  | Poleoduto ou equivalente                 |
| Verghalho com rosca total de aço, galvanizado, rosca Ø3/8" x 1225 mm de comprimento                                                                                       | Ø3/8" x 1225 mm             | 2                  | Poleoduto ou equivalente                 |
| <b>Interrompores</b>   |                             |                    |                                          |
| Conjunto montado com 1 Interruptor Paralelo, 10A 250V~, 4"2x2"   | 1P 4"2x2"                   | 1                  | Plat Legendado ou equivalente            |
| Conjunto montado com 1 Interruptor Semples 10A 250V~, 4"2x2"   | 1S 4"2x2"                   | 1                  | Plat Legendado ou equivalente            |
| Conjunto montado com 1 Interruptor de pressão, 10A 250V~, 4"2x2"   | 1B 4"2x2"                   | 1                  | Plat Legendado ou equivalente            |
| Conjunto montado de Interruptor com 2 l. cada, parafuso, 4"2x2"   | 2P 4"2x2"                   | 4                  | Plat Legendado ou equivalente            |
| Conjunto montado de Interruptor com 2 l. cada, parafuso e 1 t. cada parafuso, 4"2x2"                                                                                      | 2P+1P 4"2x2"                | 1                  | Plat Legendado ou equivalente            |
| Conjunto montado de Interruptor com 2 l. cada, parafuso e 2 t. cada parafuso, 4"2x2"                                                                                      | 2P+2P 4"2x2"                | 1                  | Plat Legendado ou equivalente            |
| Conjunto montado de Interruptor com 2 l. cada parafuso, 4"2x2"   | 3P 4"2x2"                   | 4                  | Plat Legendado ou equivalente            |
| <b>Interrompores + Tomadas</b>   |                             |                    |                                          |
| Conjunto montado de 1 Interruptor Semples + 1 Tomada 2P+1, 10A, 4"2x2"   | 1S+1Tom 10A 4"2x2"          | 1                  | Plat Legendado ou equivalente            |
| Conjunto montado de 2 Interruptores Semples + 1 Tomada 2P+1, 10A, 4"2x2"                                                                                                  | 2S + 1Tom 10A 4"2x2"        | 3                  | Plat Legendado ou equivalente            |
| Placa saída de fio   |                             |                    |                                          |
| Conjunto montado de 1 Placa para Saída de Fio Ø1" 6"2x6"   | Saída de fio                | 3                  | Plat Legendado ou equivalente            |
| <b>PVC Conduite Top</b>   |                             |                    |                                          |
| Adaptador Respingo para Conduite de Perfil, Ø1"3/4"   | Ø1" 3/4"                    | 72                 | Tigre, Linha Conduite Top ou equivalente |
| Adaptador para Conduite de Perfil, Ø1"   | Ø1"                         | 1                  | Tigre, Linha Conduite Top ou equivalente |
| Conduite de PVC multilaminado na cor cinza, Ø1", sem Tampa, com 5 entradas                                                                                                | Ø1"                         | 8                  | Tigre, Linha Conduite Top ou equivalente |
| <b>Tomadas</b>   |                             |                    |                                          |
| Caixa de Passagem no piso, com Tampa tipo unha, 4"2x2"   | 4"2x2"                      | 5                  | Blocos/Tomadas ou equivalente            |
| Conjunto montado com 2 Tomadas 2P+1, 10A, possto horizontal, 4"2x2"   | 2Tom 4"2x2"                 | 36                 | Plat Legendado ou equivalente            |
| Conjunto montado com 1 Tomada 2P+1, 10A, possto horizontal, 4"2x2"   | 1Tom 4"2x2"                 | 6                  | Plat Legendado ou equivalente            |
| Conjunto montado de 1 Tomada 2P+1, 25A, possto horizontal, 4"2x2"   | 25A 4"2x2"                  | 6                  | Plat Legendado ou equivalente            |
| Grand total: 1527   |                             | 1527               |                                          |

| Quantitativo de Eletrocalhas                          |             |                           |
|-------------------------------------------------------|-------------|---------------------------|
| Tipo                                                  | Dimensões   | Comprimento Corrigido (m) |
| Eletrocalha Perfurada Galvanizada à Quente - Genérica | 50 x 50 mm  | 15,14 m                   |
| Eletrocalha Perfurada Galvanizada à Quente - Genérica | 50 x 100 mm | 11,68 m                   |
| Perfildado Perfurado 38x38mm-Niedax-MOPA              | 38 x 38 mm  | 34,60 m                   |
| Grand total: 77                                       |             | 61,41 m                   |

|                                                                                       |             |                                                                                       |                       |
|---------------------------------------------------------------------------------------|-------------|---------------------------------------------------------------------------------------|-----------------------|
| 00                                                                                    | 12/09/2026  | Emissão Inicial                                                                       |                       |
| <b>Número</b>                                                                         | <b>Data</b> | <b>Descrição da revisão</b>                                                           |                       |
| <b>Tabela de revisões</b>                                                             |             |                                                                                       |                       |
| Eng. Suelio L. de Alencar<br><b>CREA: 112061738-3</b>                                 |             | Aluno Migrando Para BIM 2.0<br><b>CPF/CNPJ: xxx.xxx000.xxx0000/xx</b>                 |                       |
| <h1>DIAGRAMAS E QUANTITATIVOS</h1>                                                    |             |                                                                                       |                       |
|  |             |  |                       |
| <b>Migrando para BIM</b><br>com Revit + Pro-Elétrica                                  |             | <b>ELÉTRICA 2.0</b>                                                                   |                       |
| <b>Projeto</b><br>Migrando para Bim 2.0                                               |             |                                                                                       |                       |
| <b>Proprietário</b><br>Aluno Migrando Para BIM 2.0                                    |             |                                                                                       |                       |
| <b>Endereço</b><br>Preencha aqui o endereço                                           |             |                                                                                       |                       |
| <b>Conteúdo:</b><br>Diagramas, Tabelas de Painéis e Quantitativos                     |             | <b>Pavimento</b><br>Escala INDICADA<br><b>Projelista</b><br>Suelio L. de Alencar      | <b>FOLHA</b><br>3 / 4 |
| <b>Disciplina</b><br>Elétrica                                                         |             | <b>Data</b><br>09/12/26                                                               |                       |