




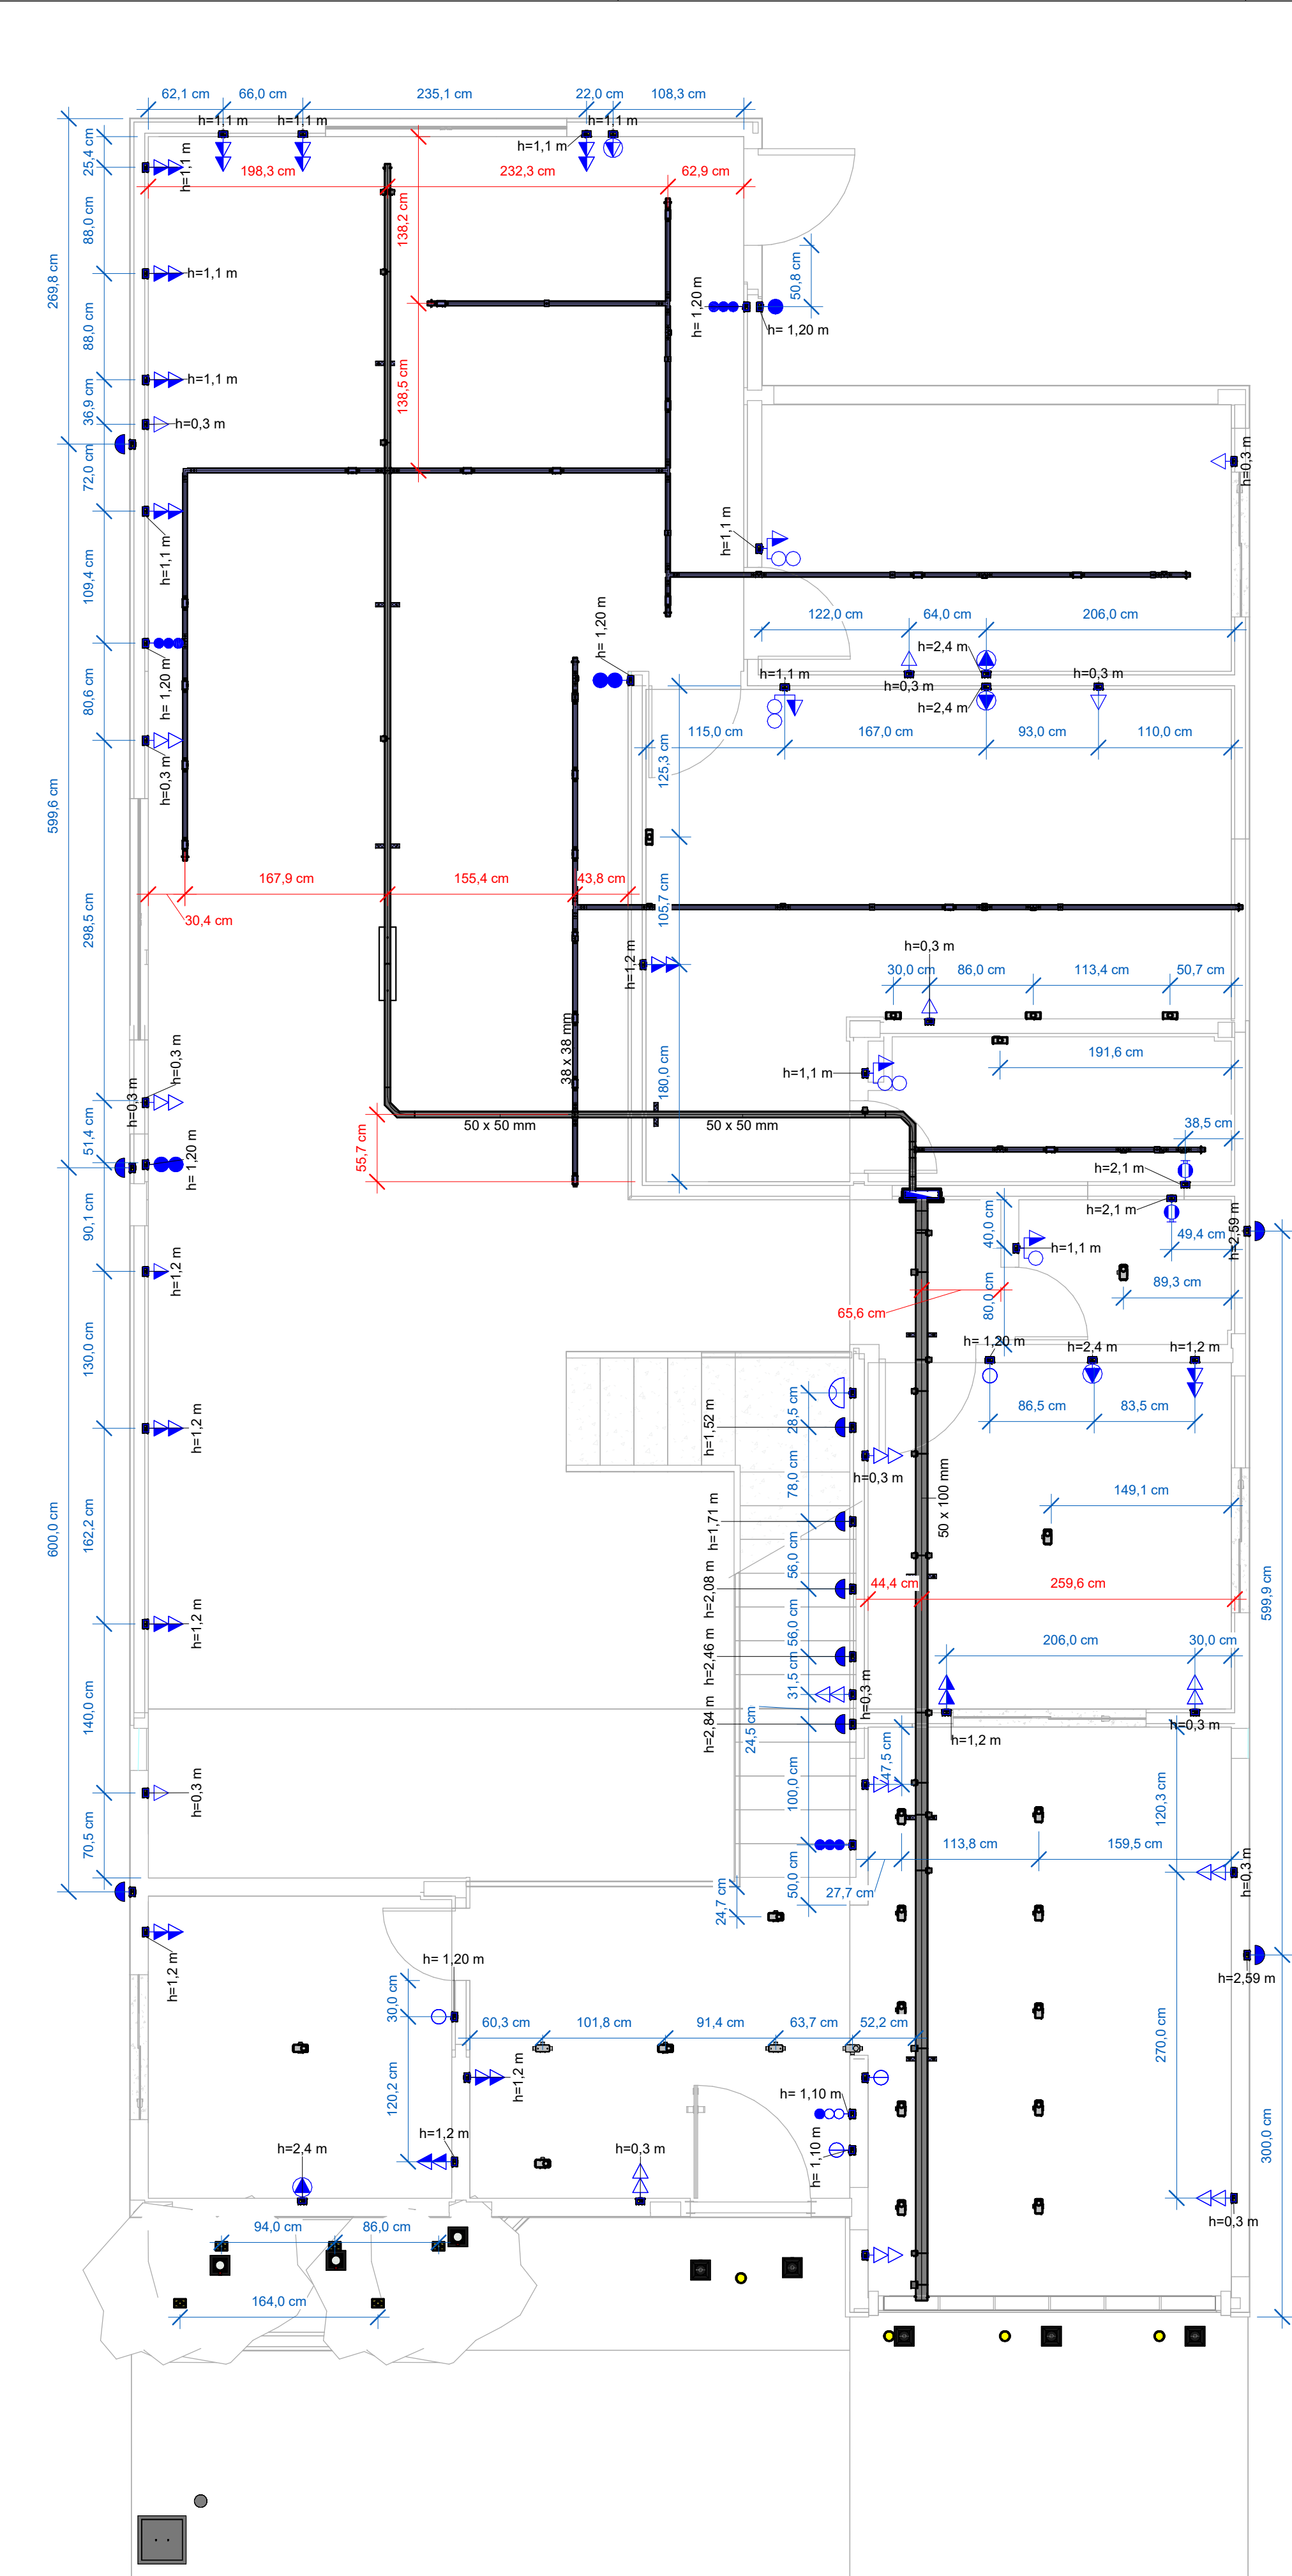


1 TÉRREO-ELT LAYOUT
1 : 40

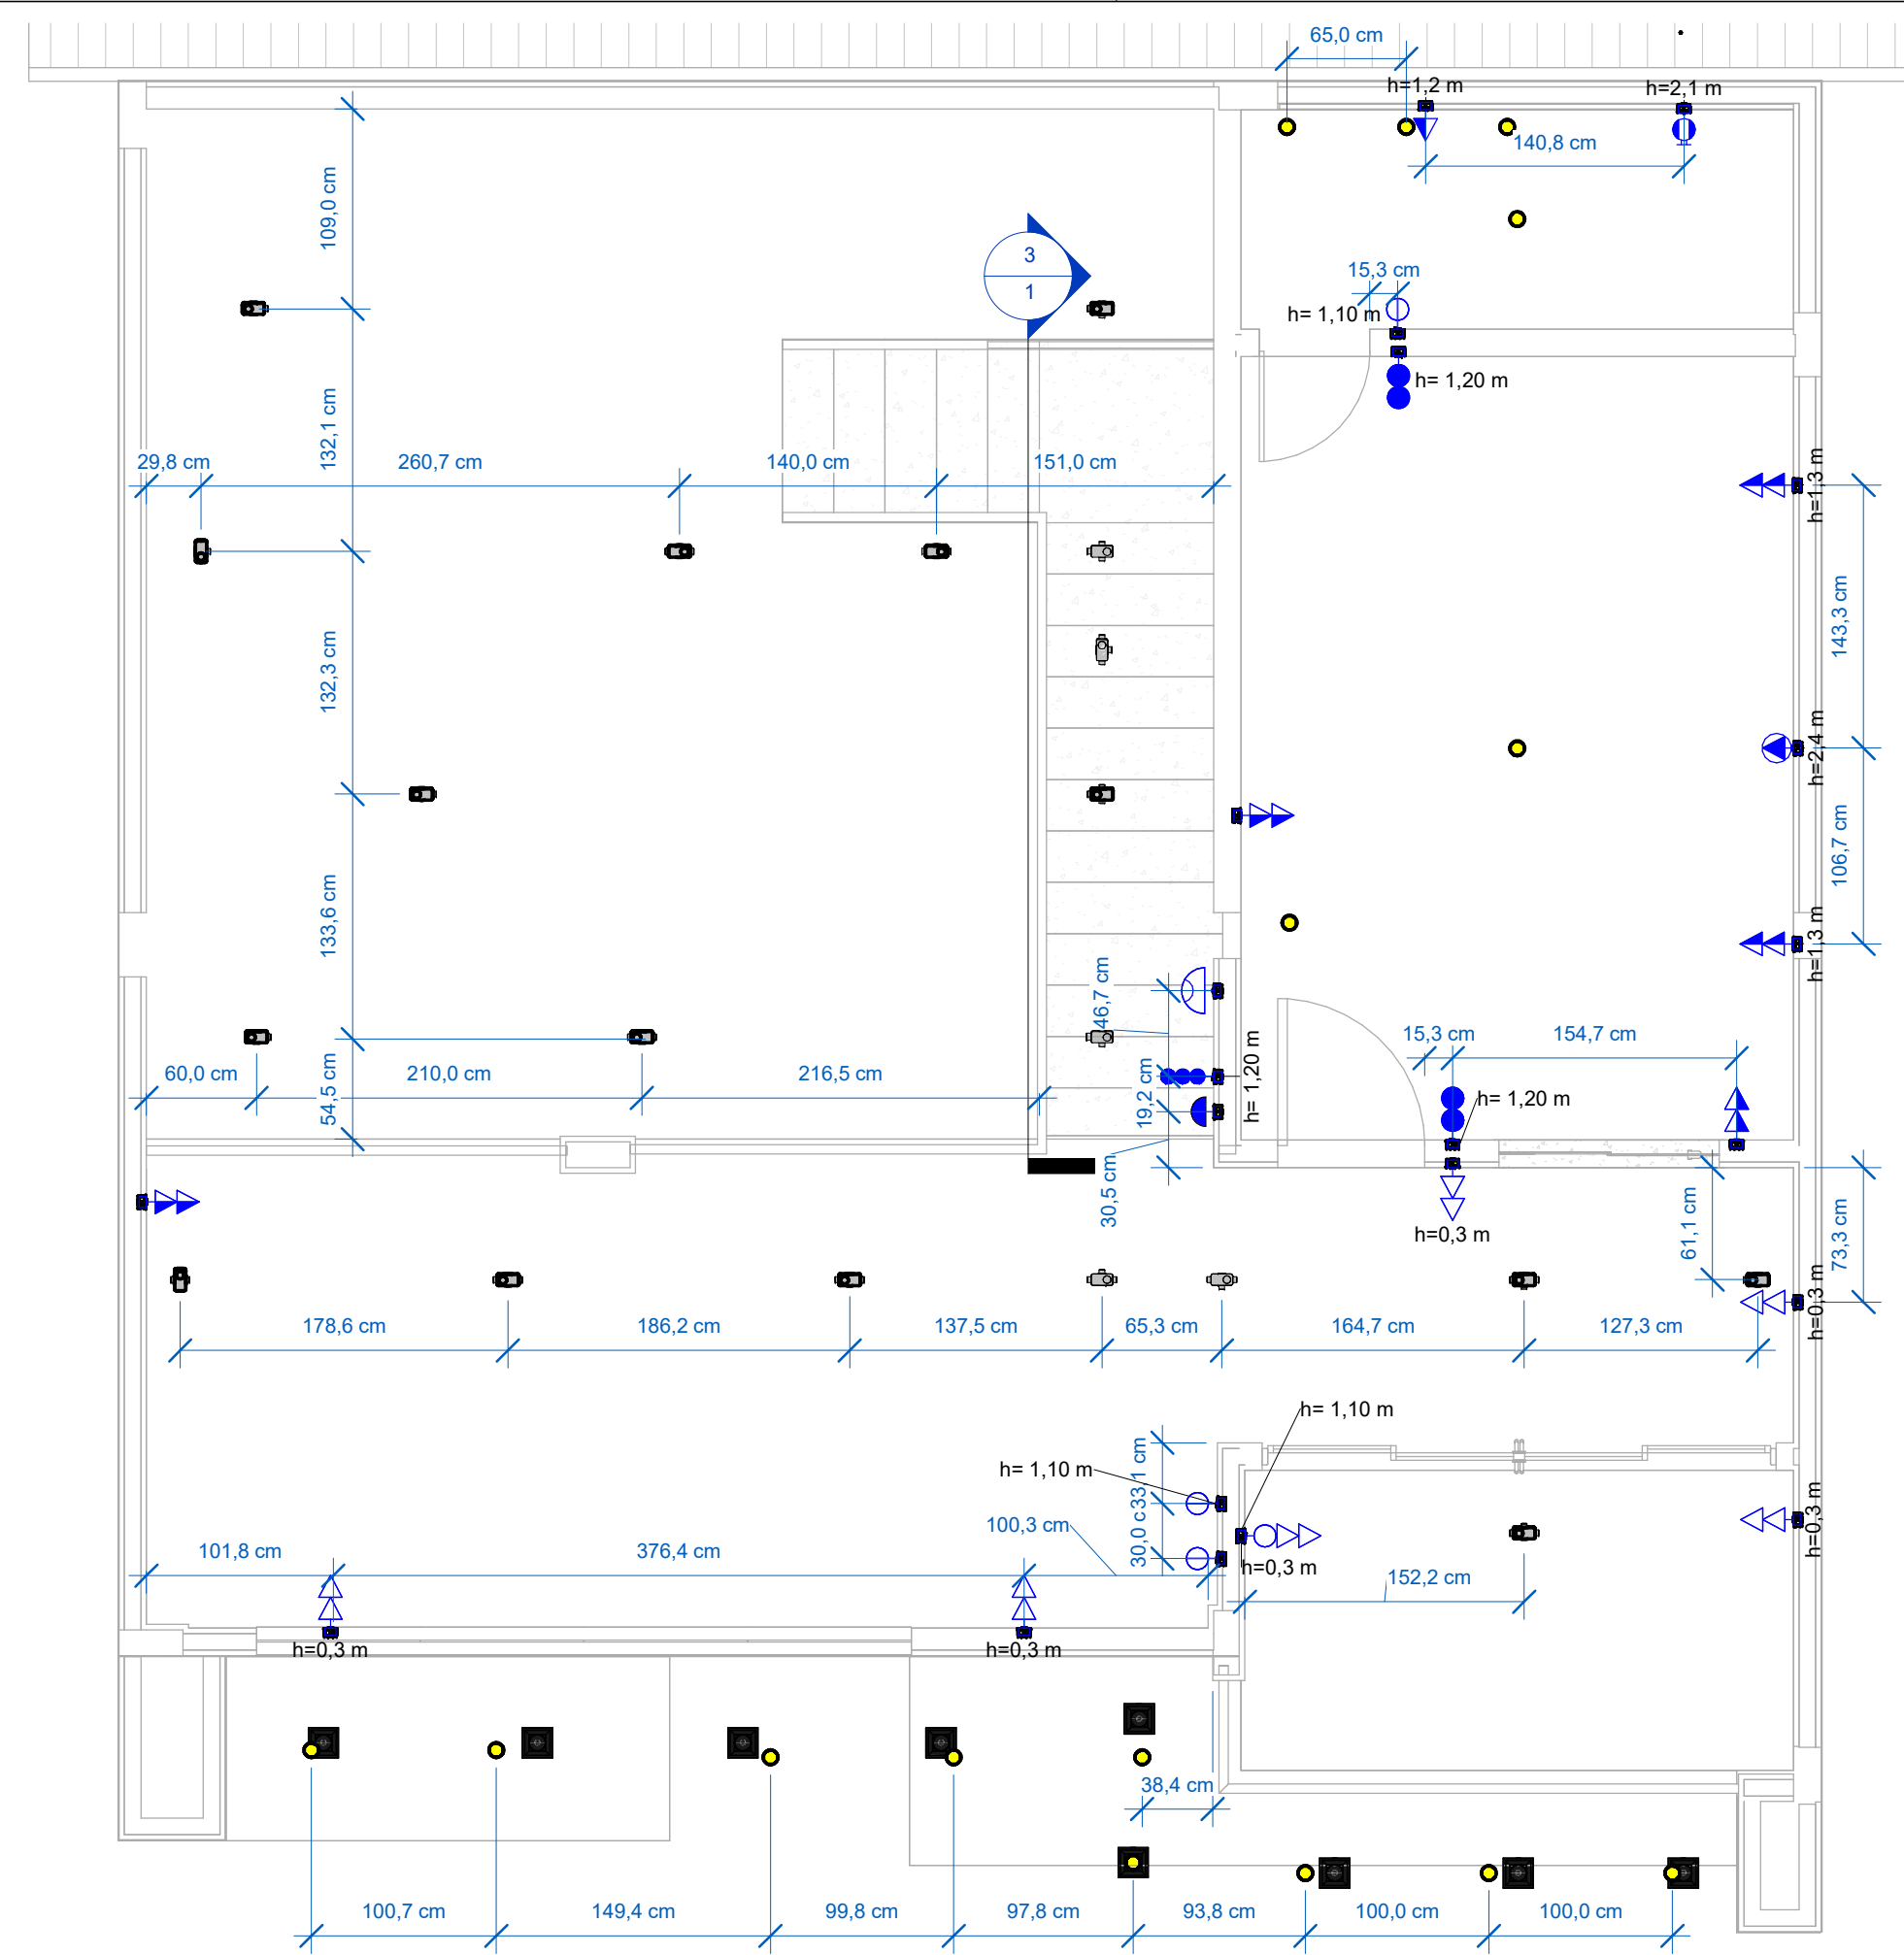


2 SUPERIOR-ELT LAYOUT
1 : 40

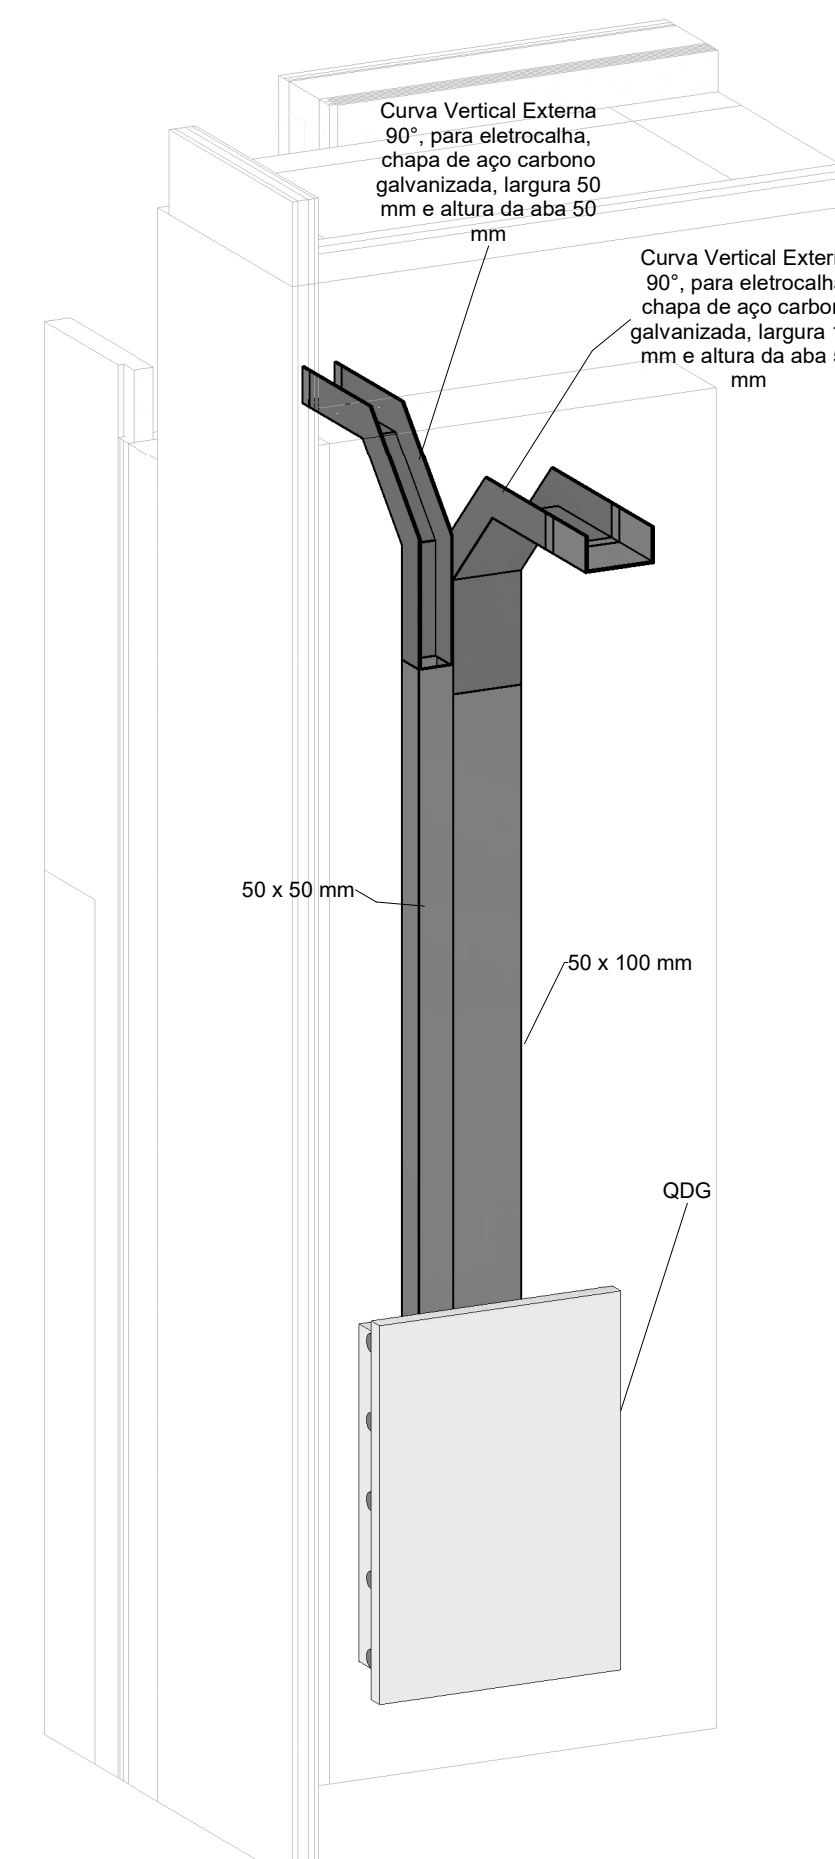

3 3D SAÍDA QUADRO

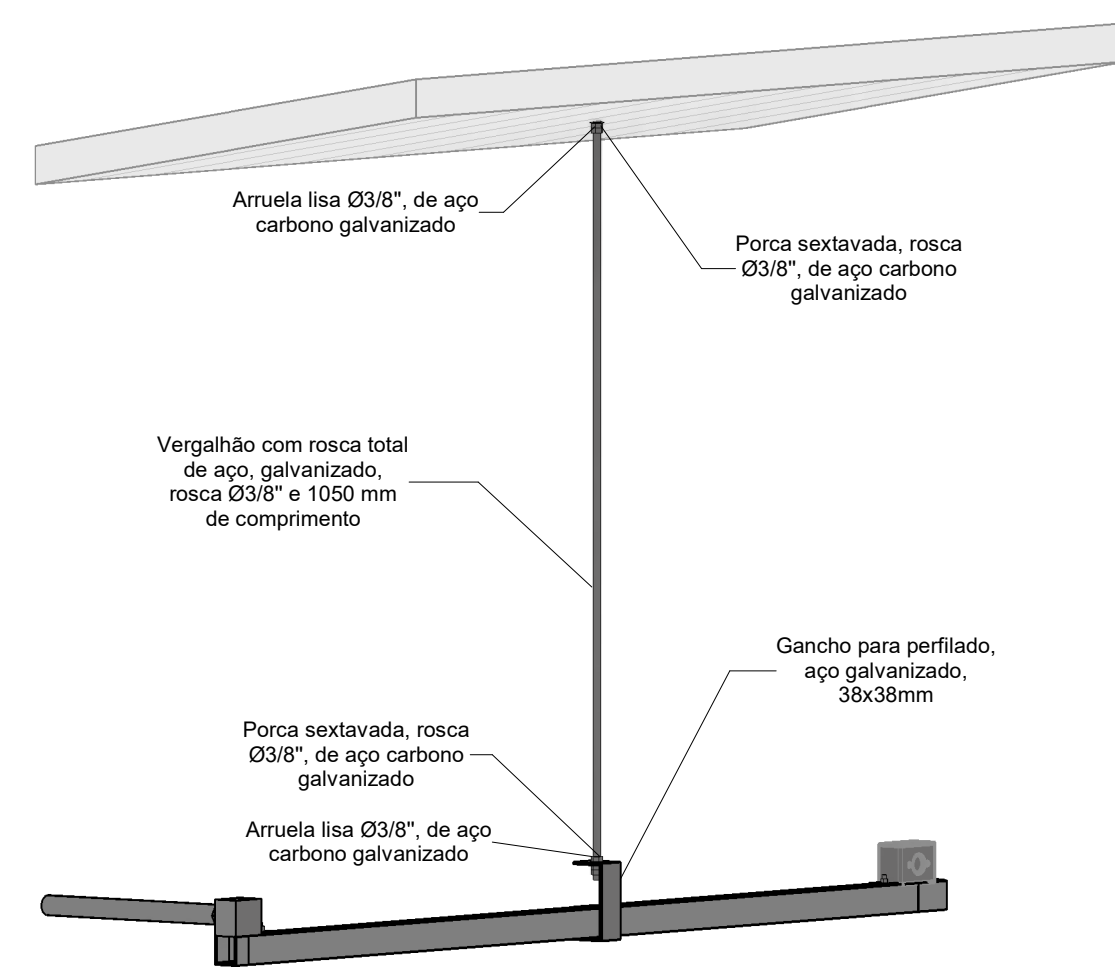

5 DETALHE SUPORTE PERFILADO

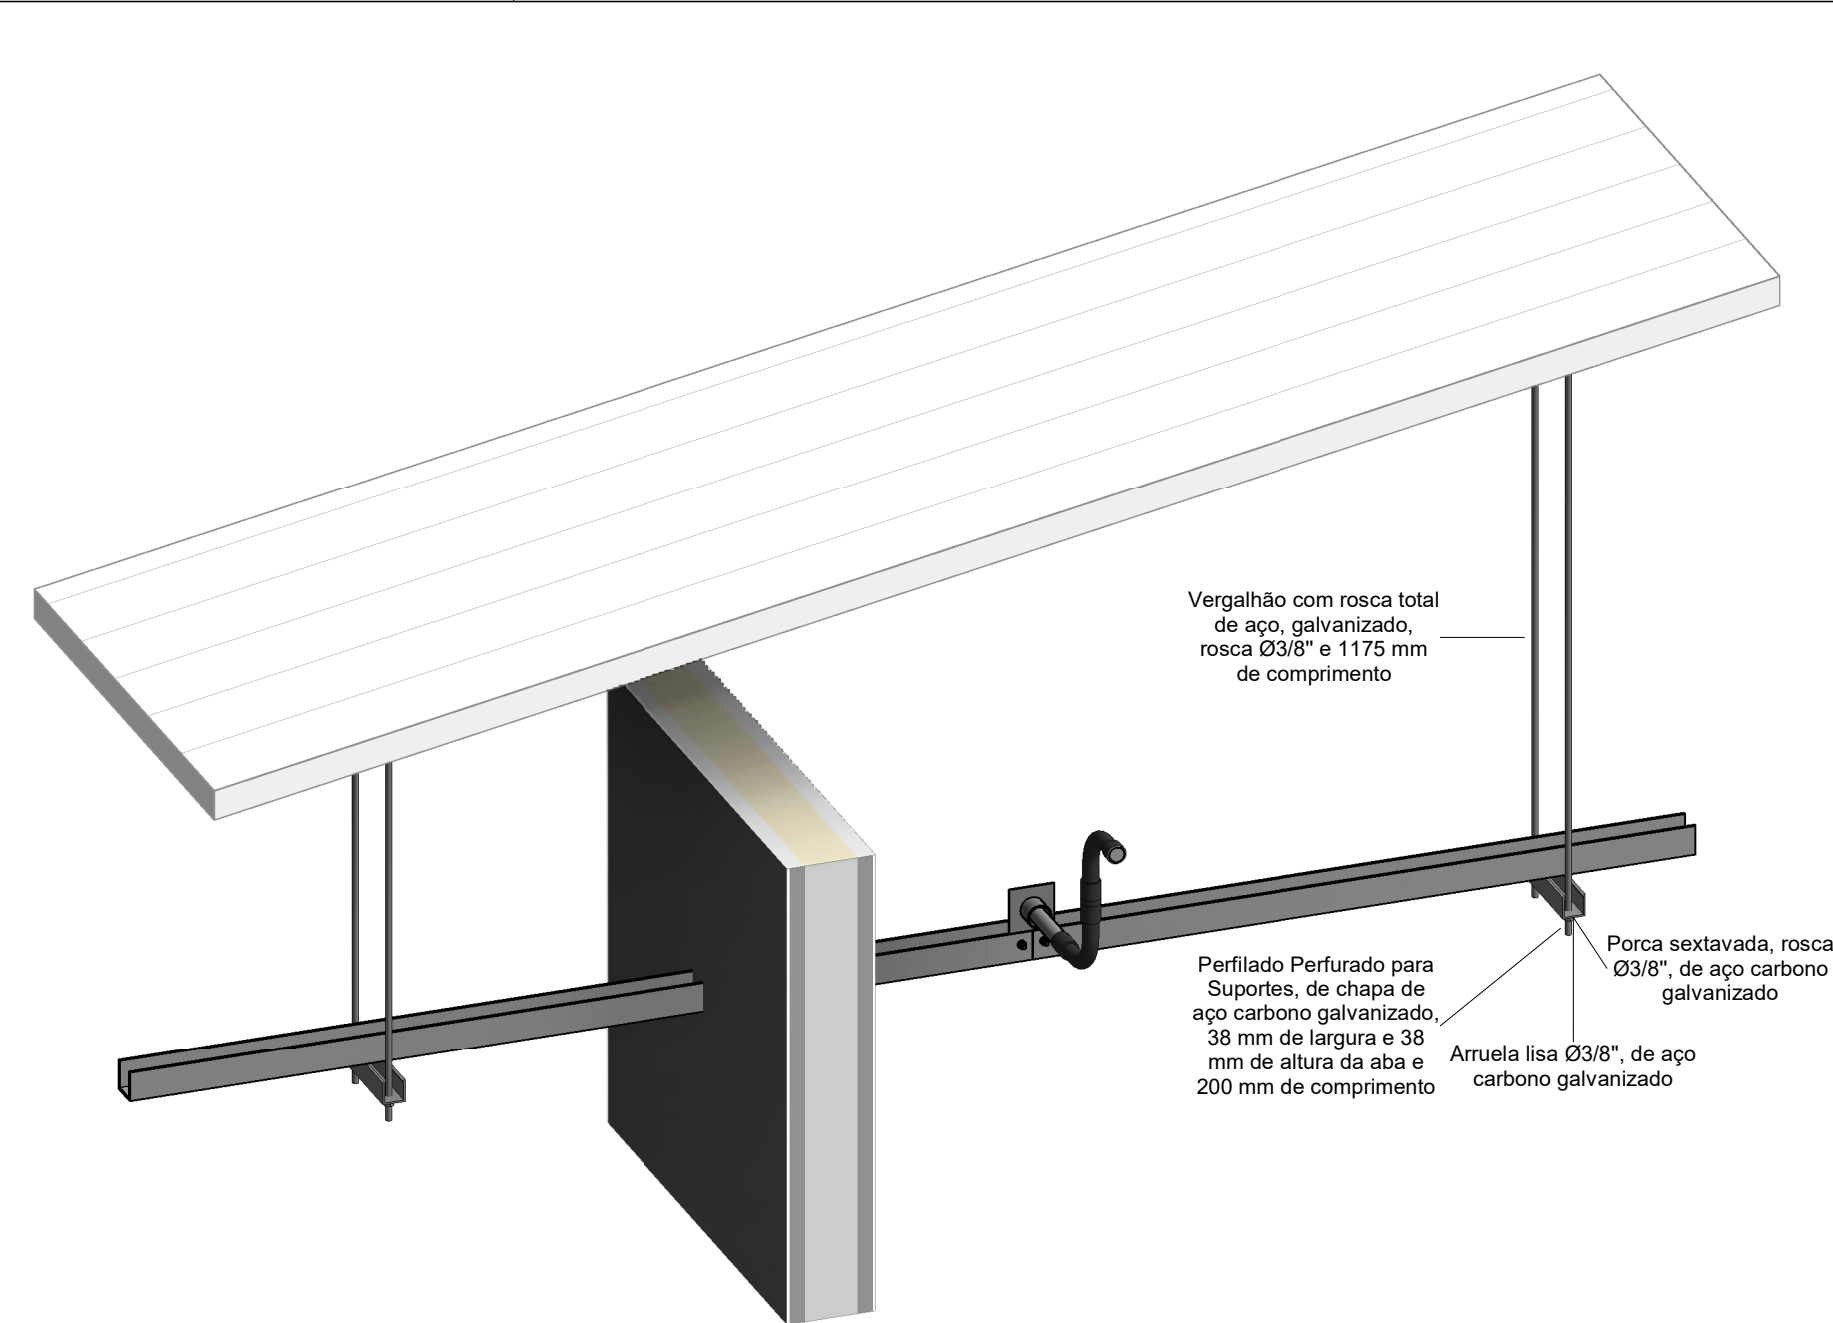

4 DETALHE SUPORTES ELETROCALHAS

00	12/09/2026	Emissão Inicial
Número	Data	Descrição da revisão
Tabela de revisões		
Eng. Suélio L. de Alencar CREA: 112061738-3		Aluno Migrando Para BIM 2.0 CPF/CNPJ: xxx.xxxx.xxxx/xx
LAYOUT E DETALHES		
 		
Projeto Migrando para Bim 2.0		
Proprietário Aluno Migrando Para BIM 2.0		
Endereço Preencha aqui o endereço		
Conteúdo: Plantas de Layout e Detalhes		Pavimento Escala INDICADA Projeto Suélio L. de Alencar Data 09/12/26
Disciplina Elétrica		FOLHA 2 4